



1 Implantação
1 : 200

2 Térreo
1 : 50

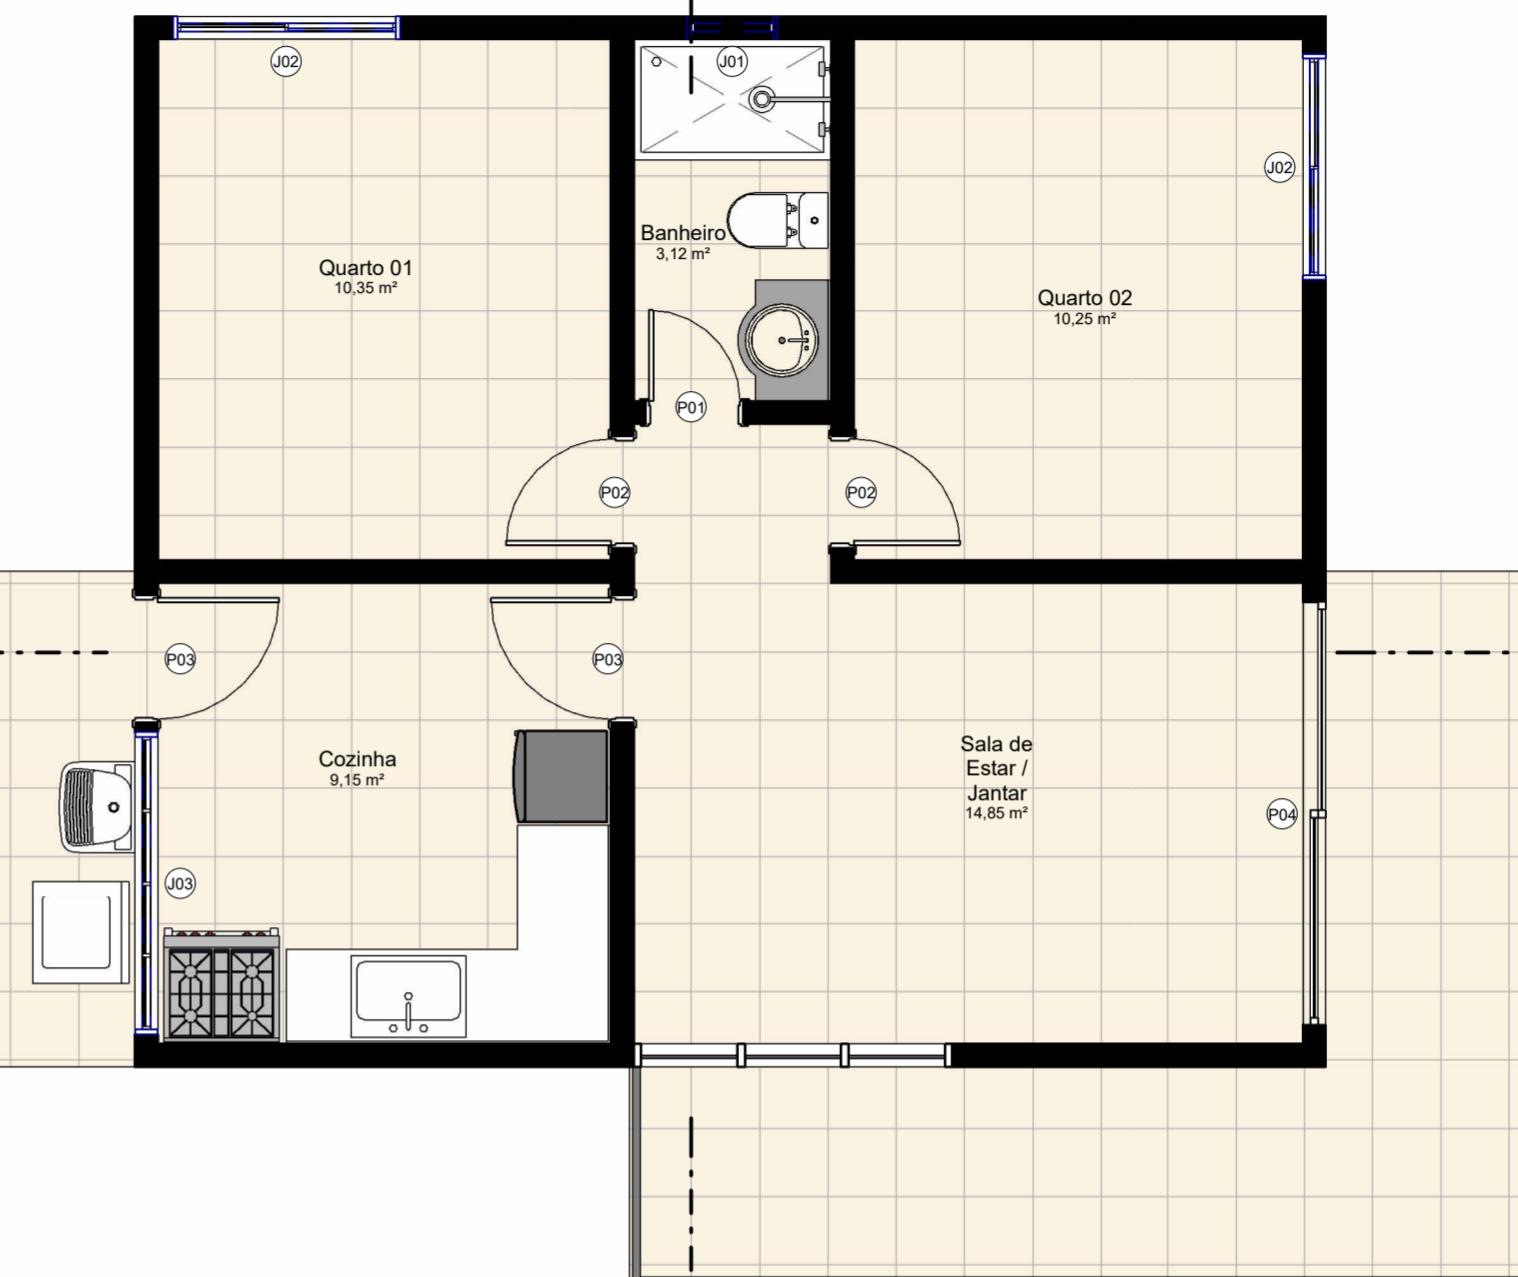


Ambientes do Projeto	
Nome	Área
Banheiro	3,12 m ²
Cozinha	9,15 m ²
Quarto 01	10,35 m ²
Quarto 02	10,25 m ²
Sala de Estar / Jantar	14,85 m ²
47,71 m ²	

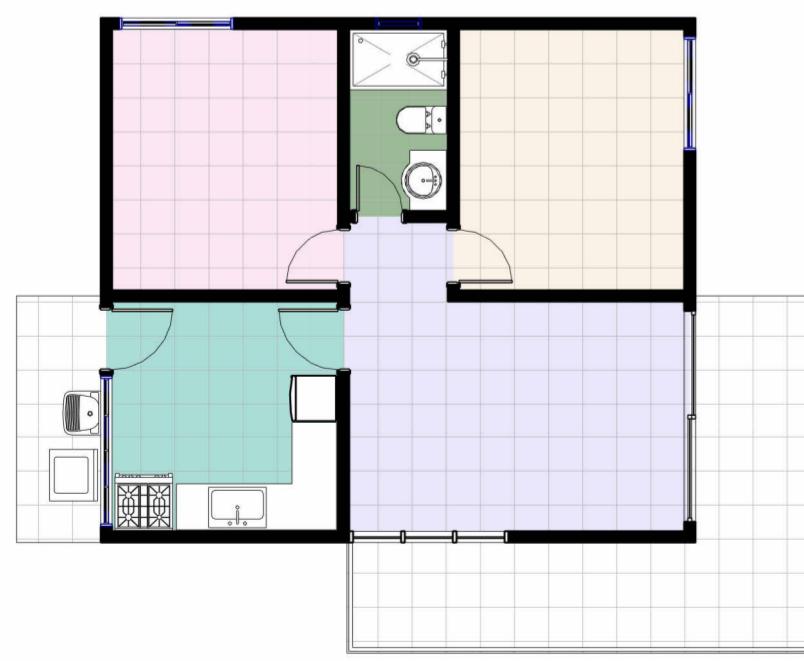

3 Ambientes
1 : 100

Ambientes

- Cozinha
- Banheiro
- Quarto 01
- Quarto 02
- Sala de Estar / Jantar

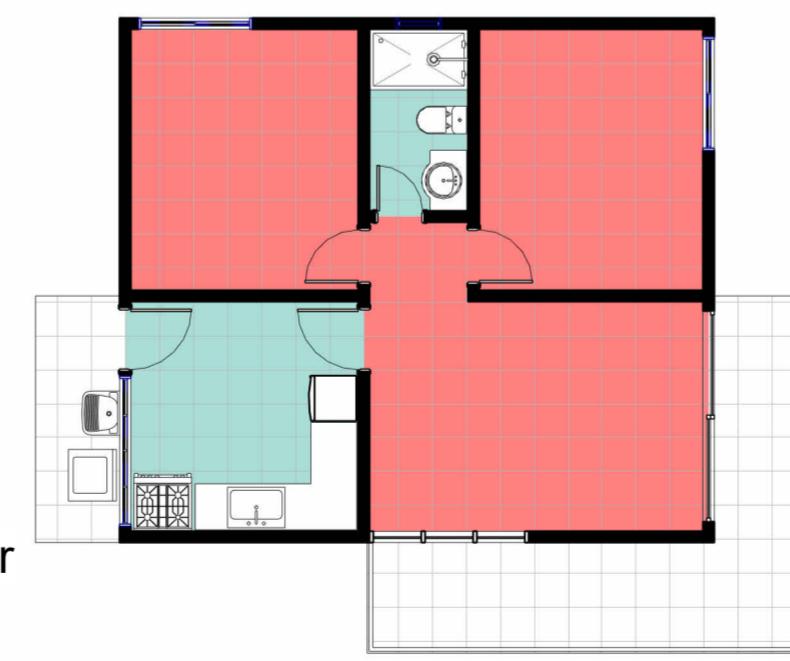

4 Departamentos
1 : 100

Setores

- Área Molhada
- Área Seca


Tabela de Portas				
Código	Dimensões (m)		Descrição	Quantidade
	Largura	Altura		
P01	0,64	2,12	Porta de Abrir - 1 Folha	1
P02	0,74	2,12	Porta de Abrir - 1 Folha	2
P03	0,84	2,12	Porta de Abrir - 1 Folha	2
P04	2,80	2,10	Porta de correr de vidro - 2 Folhas	1

Tabela de Janelas					
Código	Dimensões (m)			Descrição	Quantidade
	Largura	Altura	Alt. Peitoril		
J01	0,60	0,60	1,50	Janela Maxim-ar - 1 Folha	1
J02	1,50	1,20	0,90	Janela de correr - 2 Folhas	2
J03	2,00	1,20	0,90	Janela de correr - 4 Folhas	1

 **axiom**
Projetos e Treinamentos


Axiom Treinamentos	
Aula Experimental de Revit	
Prof.: Erick Mark	00/00/0000
Plantas Baixas	Escala Indicada

02
06

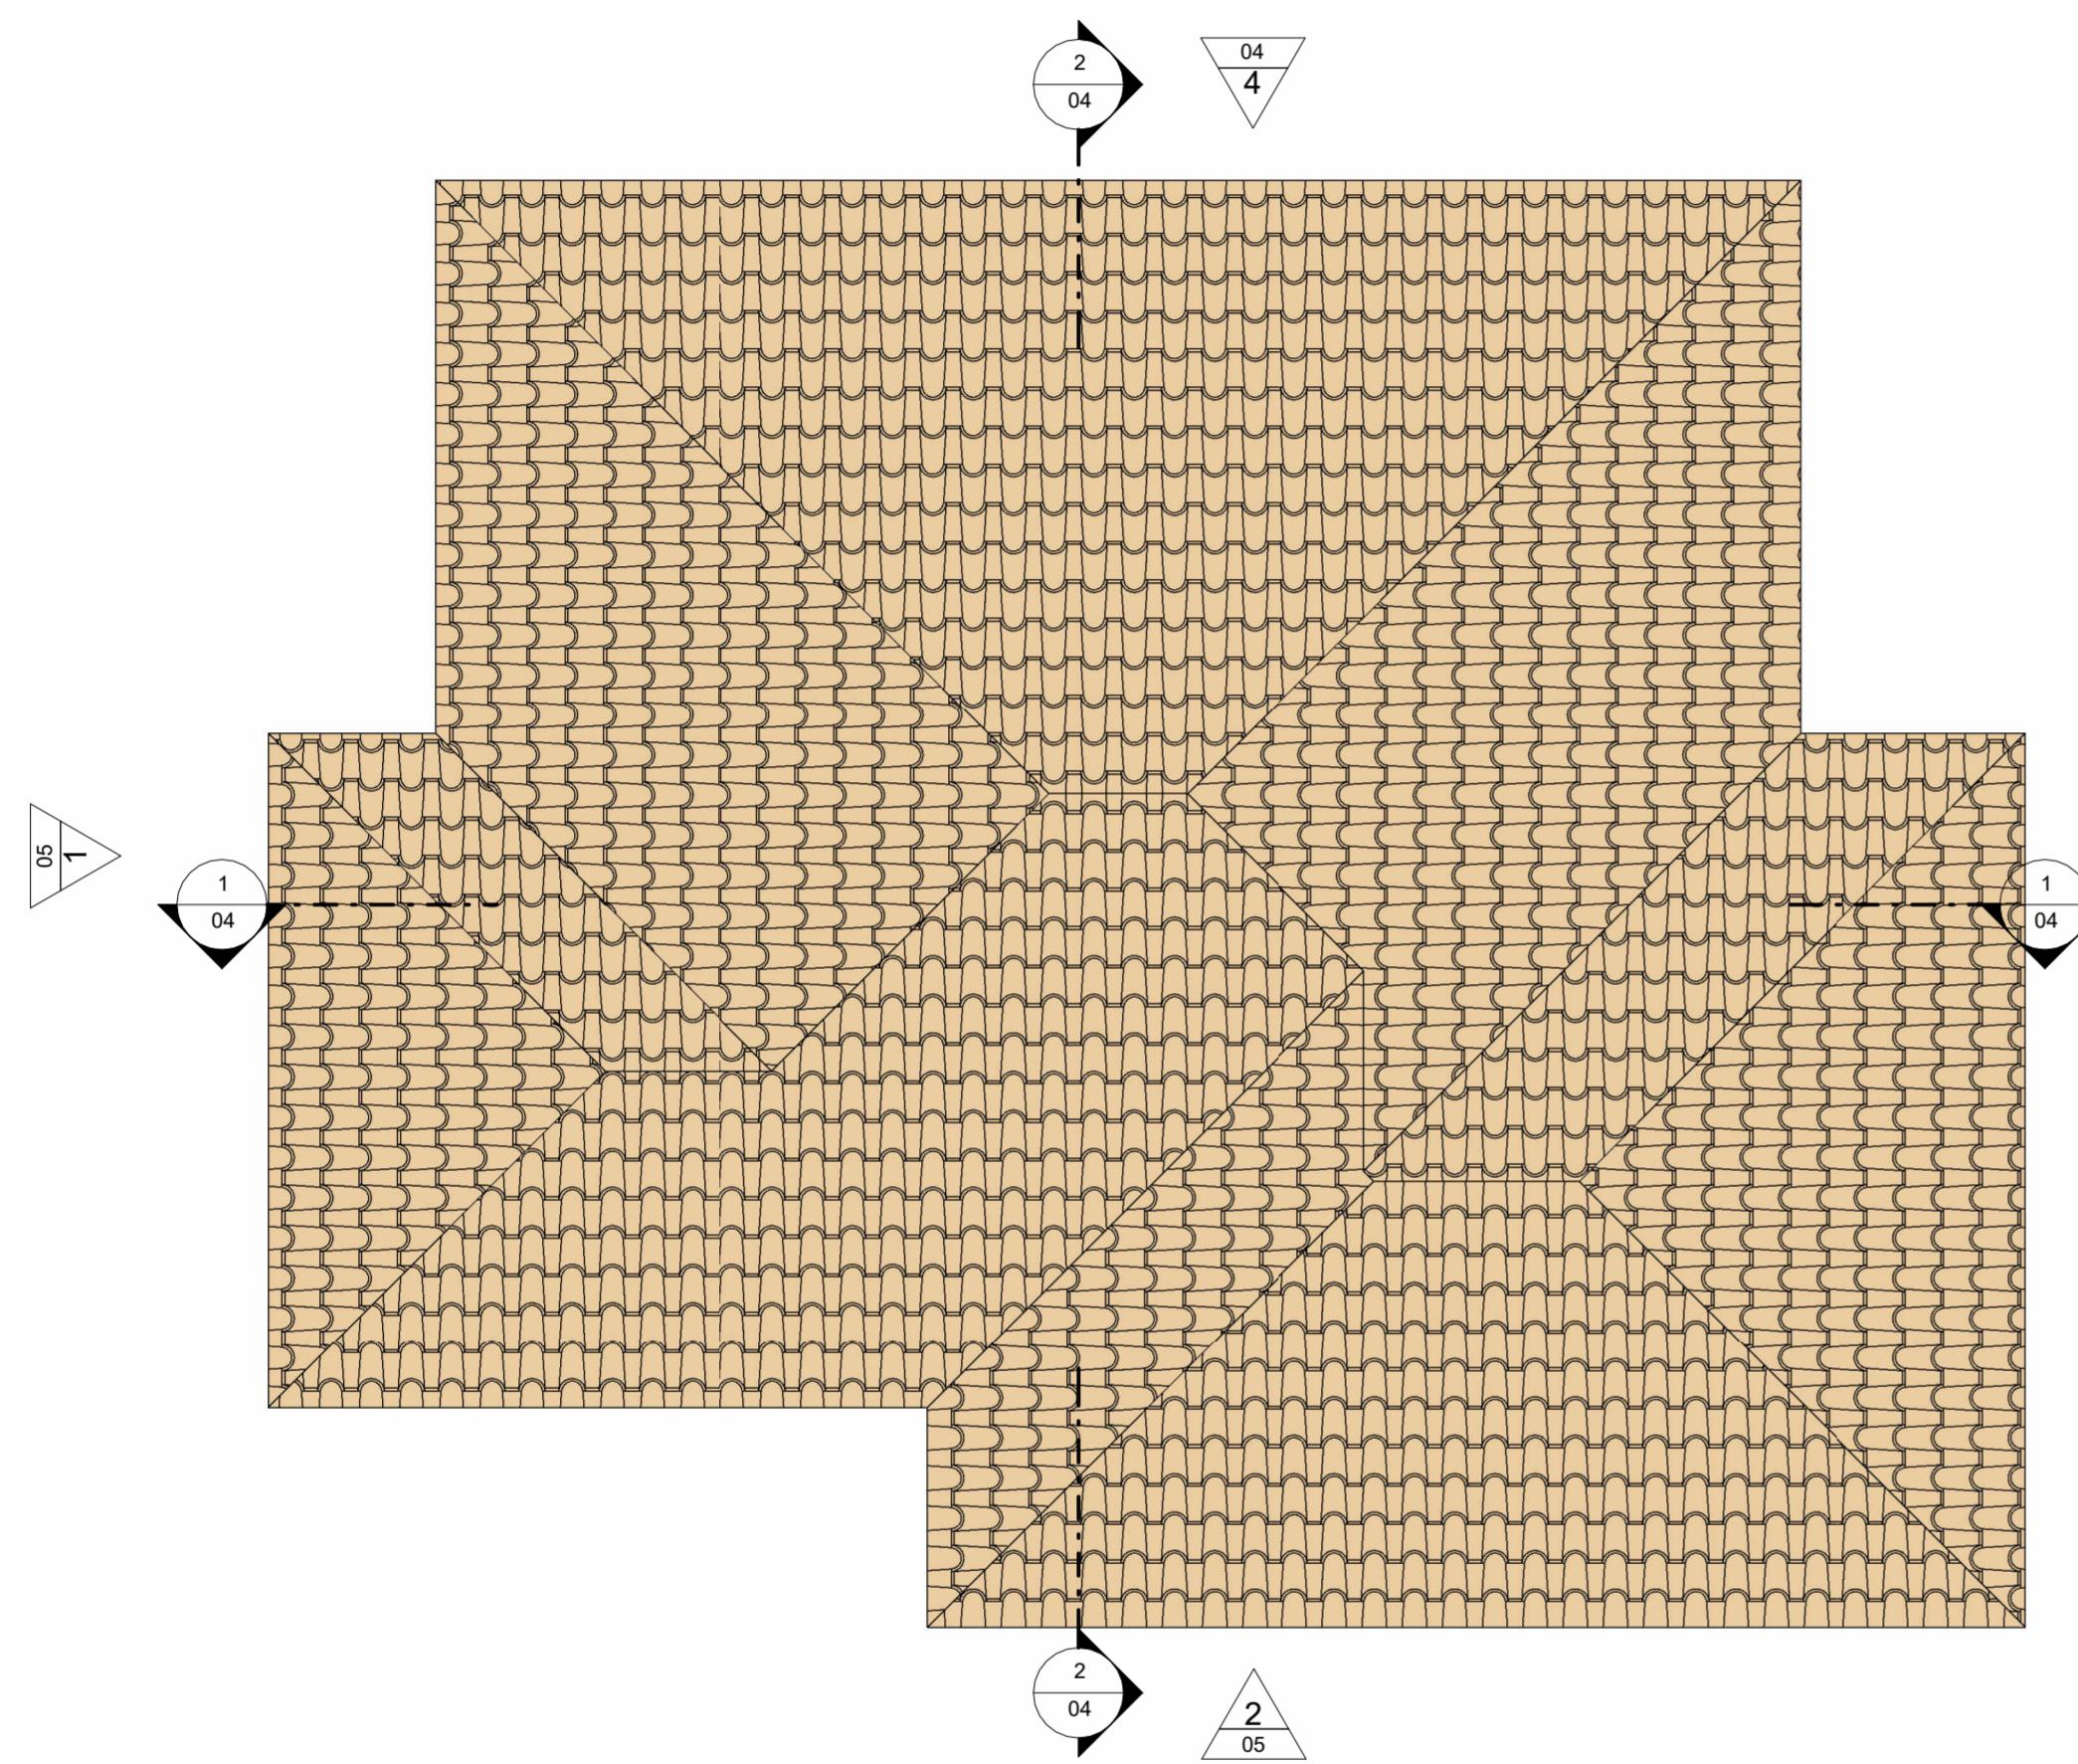


1 Cobertura


1 : 50

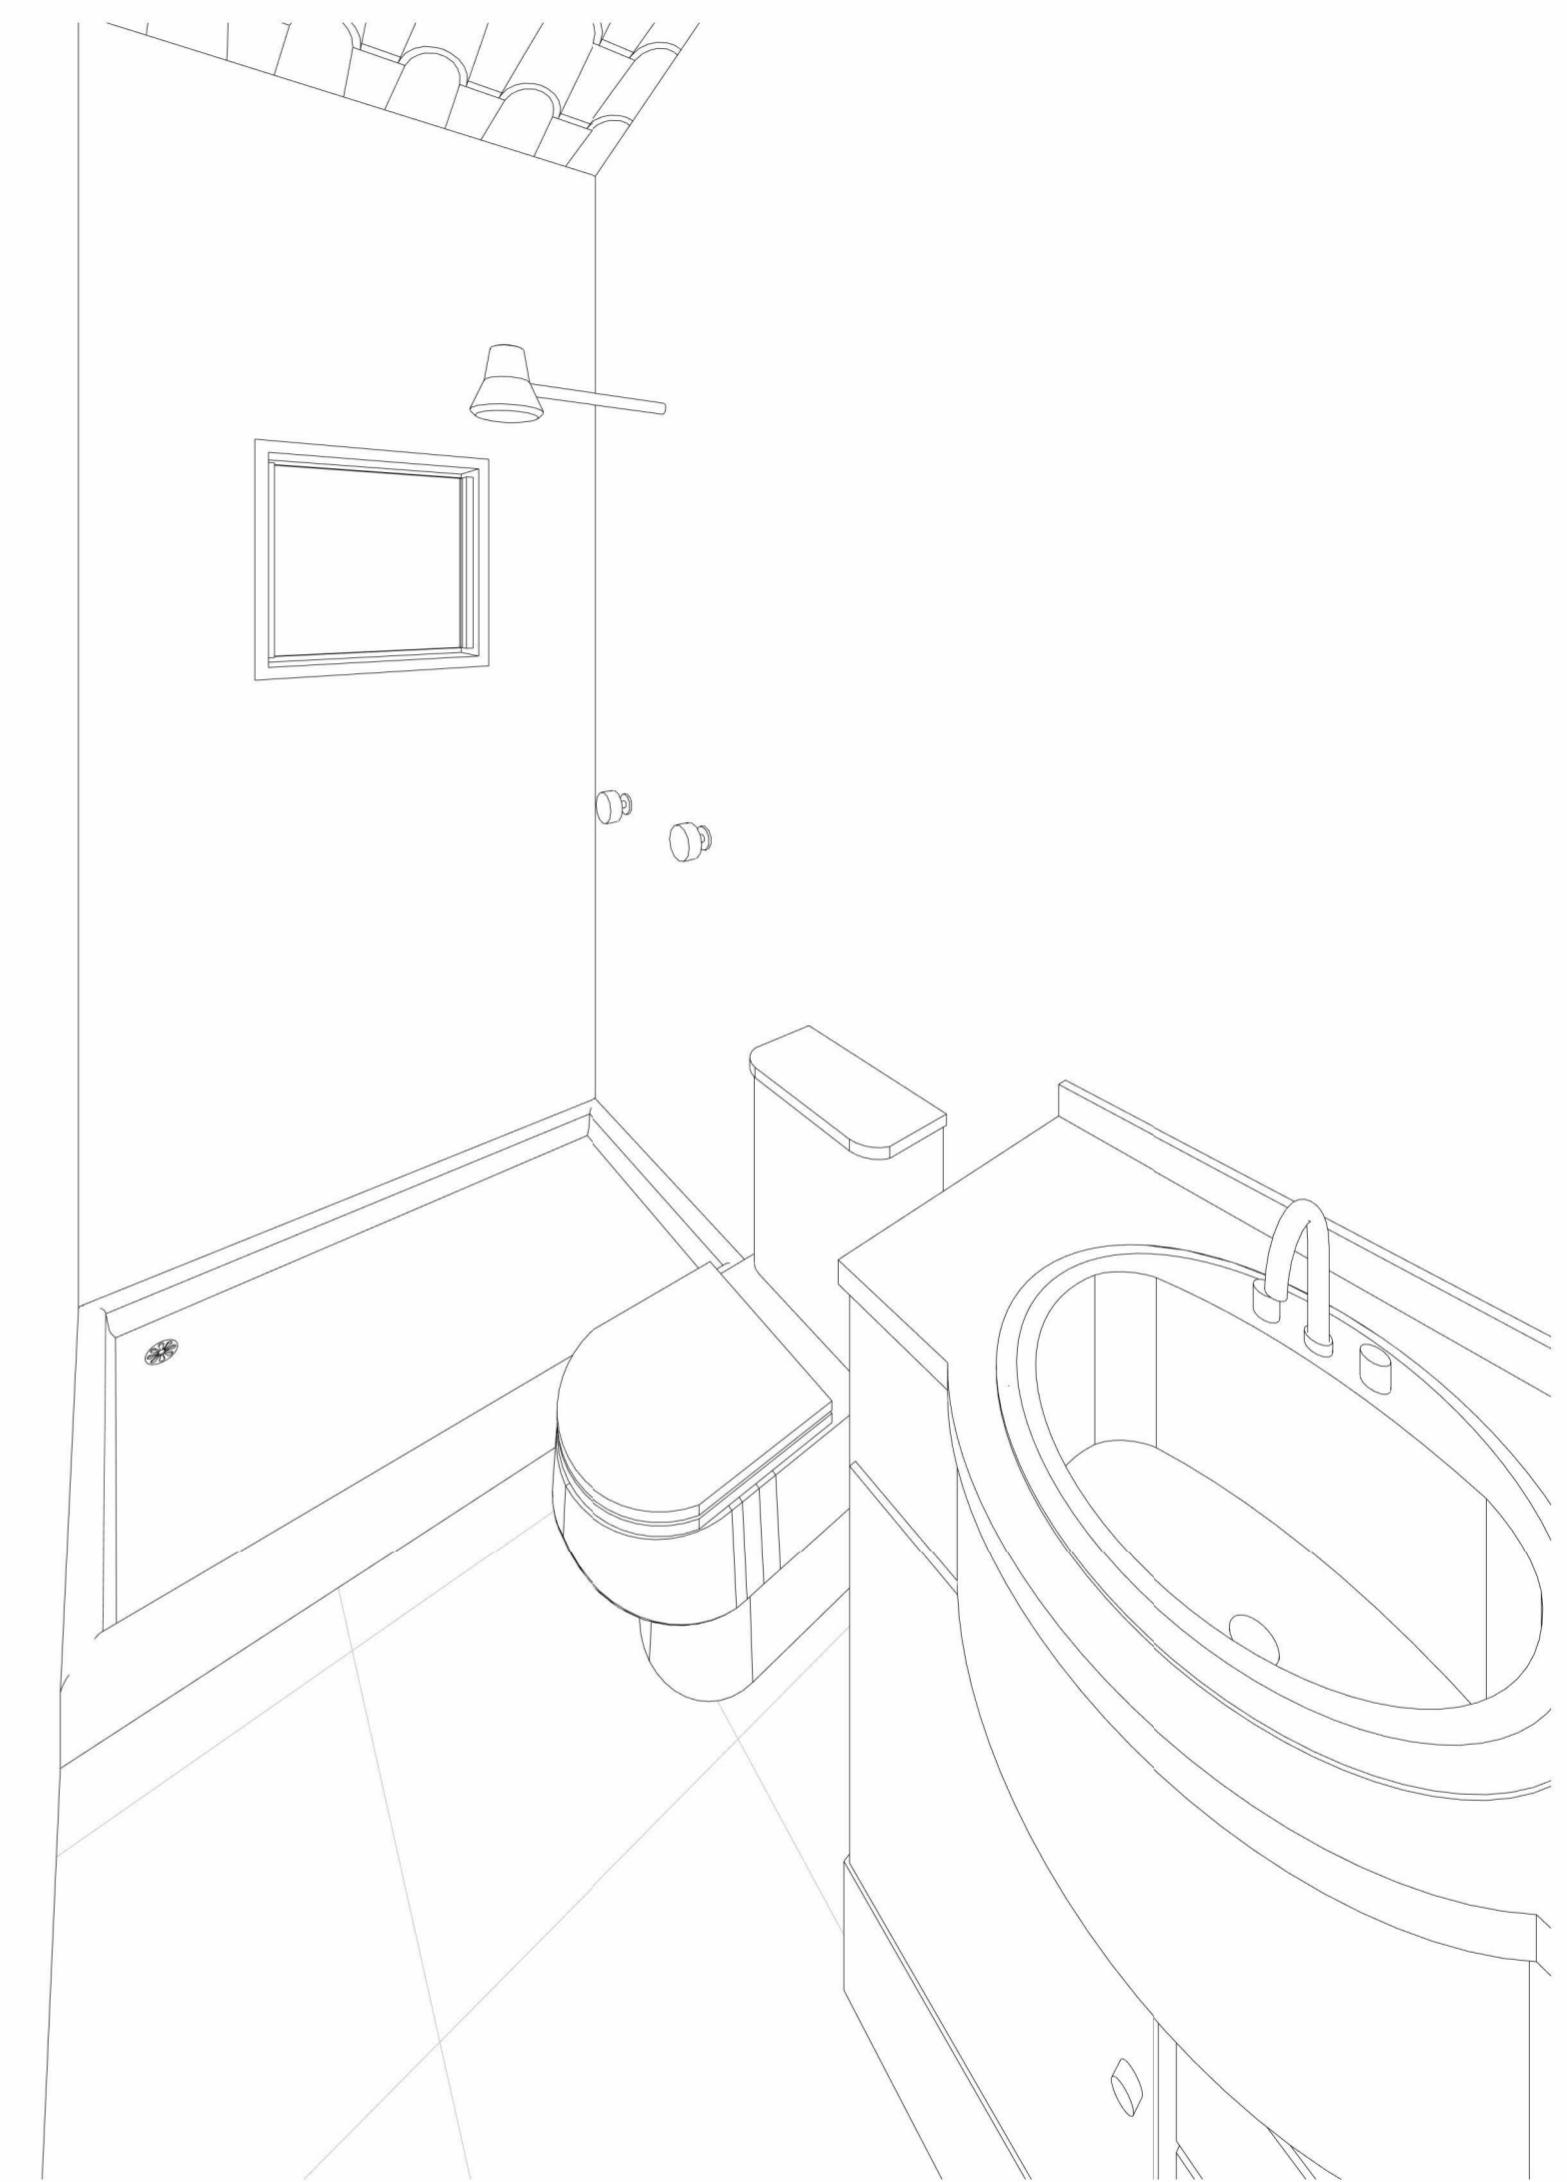

2 Perspectiva Banheiro

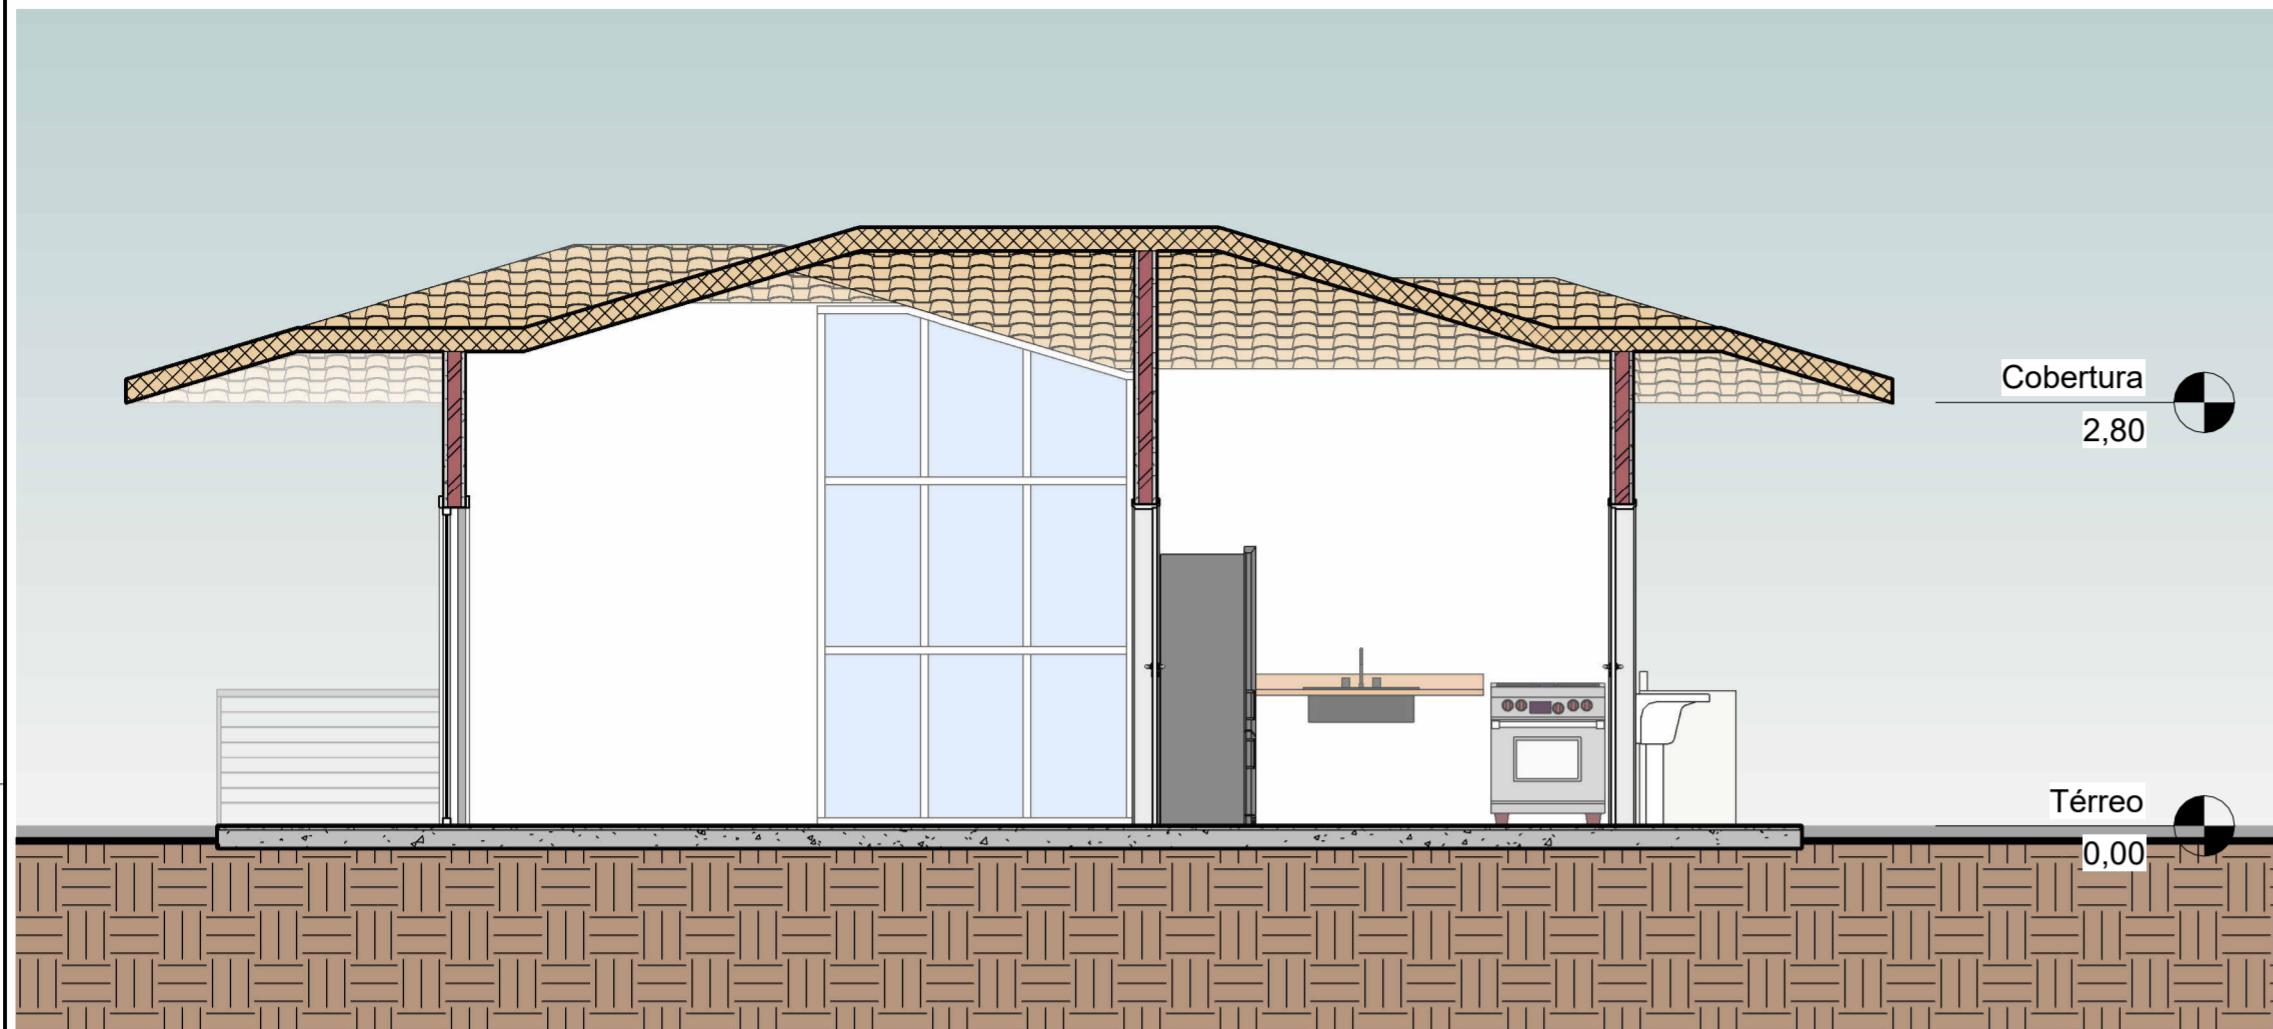


1 Corte 01
1 : 50

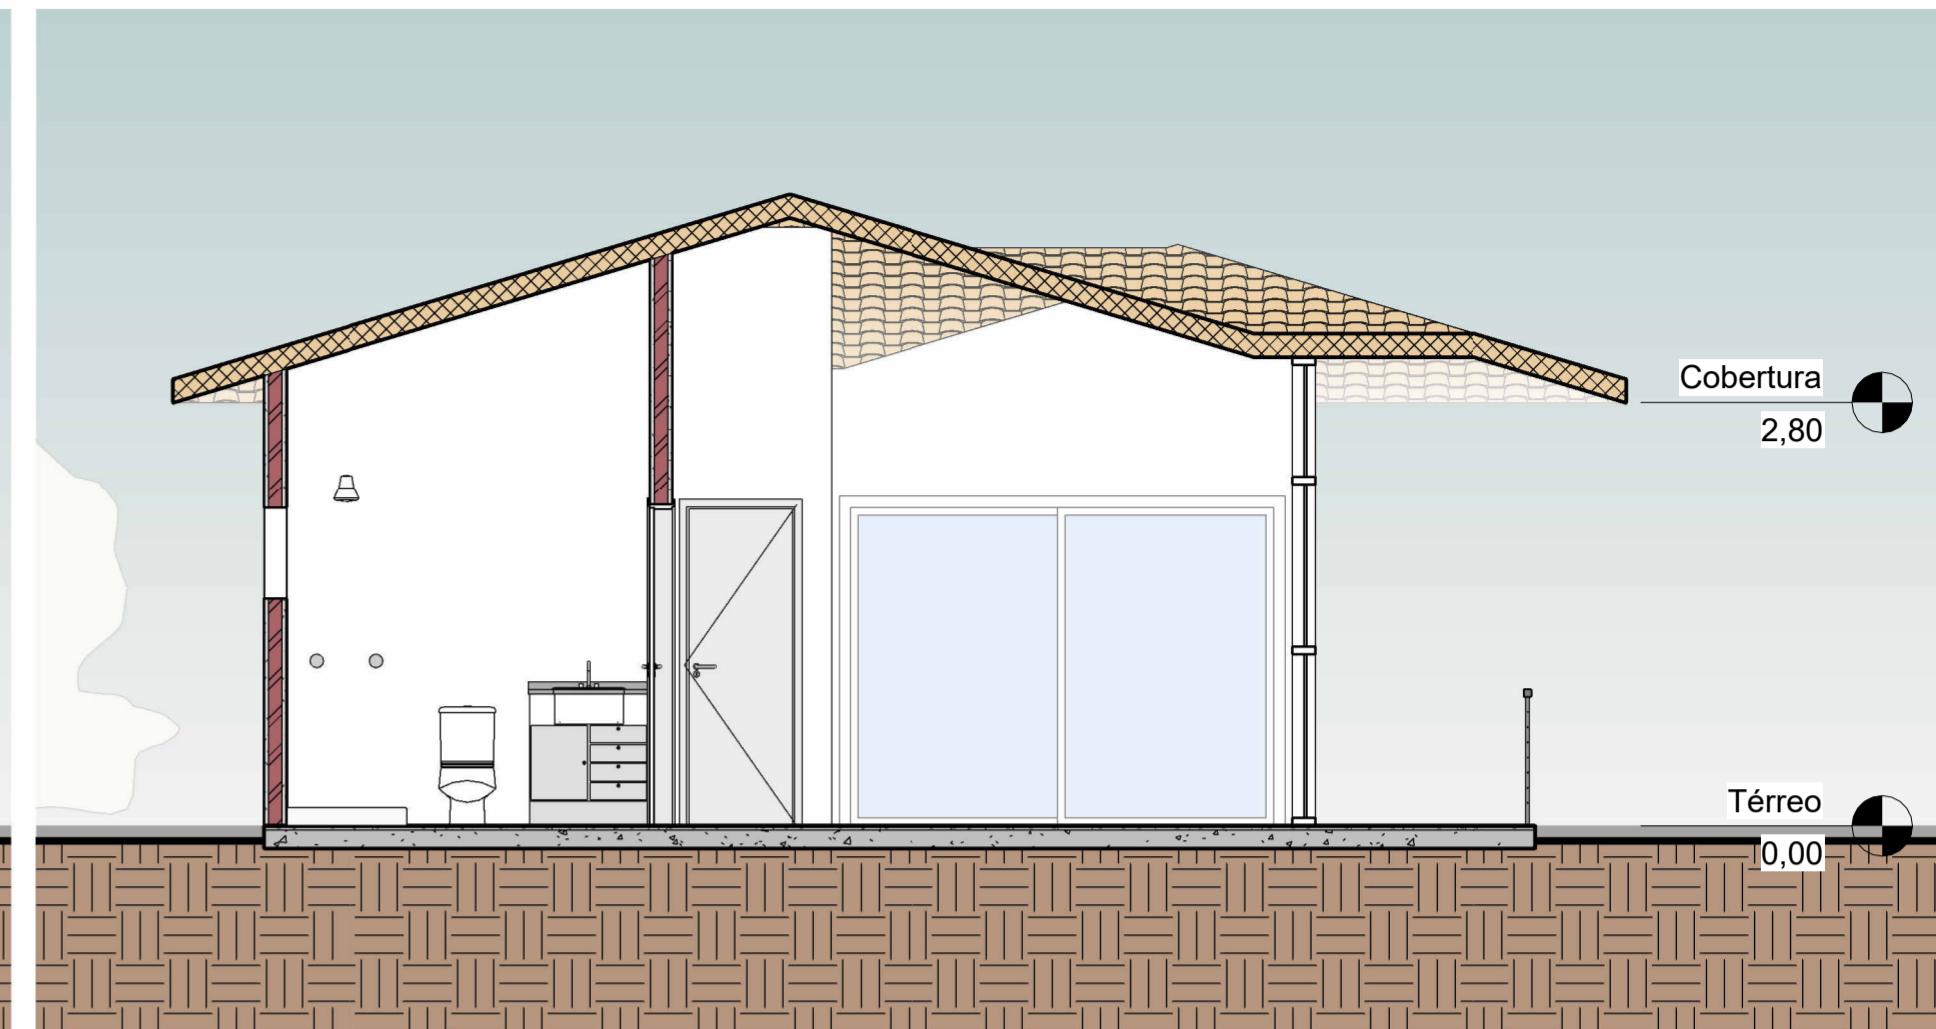


2 Corte 02
1 : 50



3 Elevação Leste
1 : 100

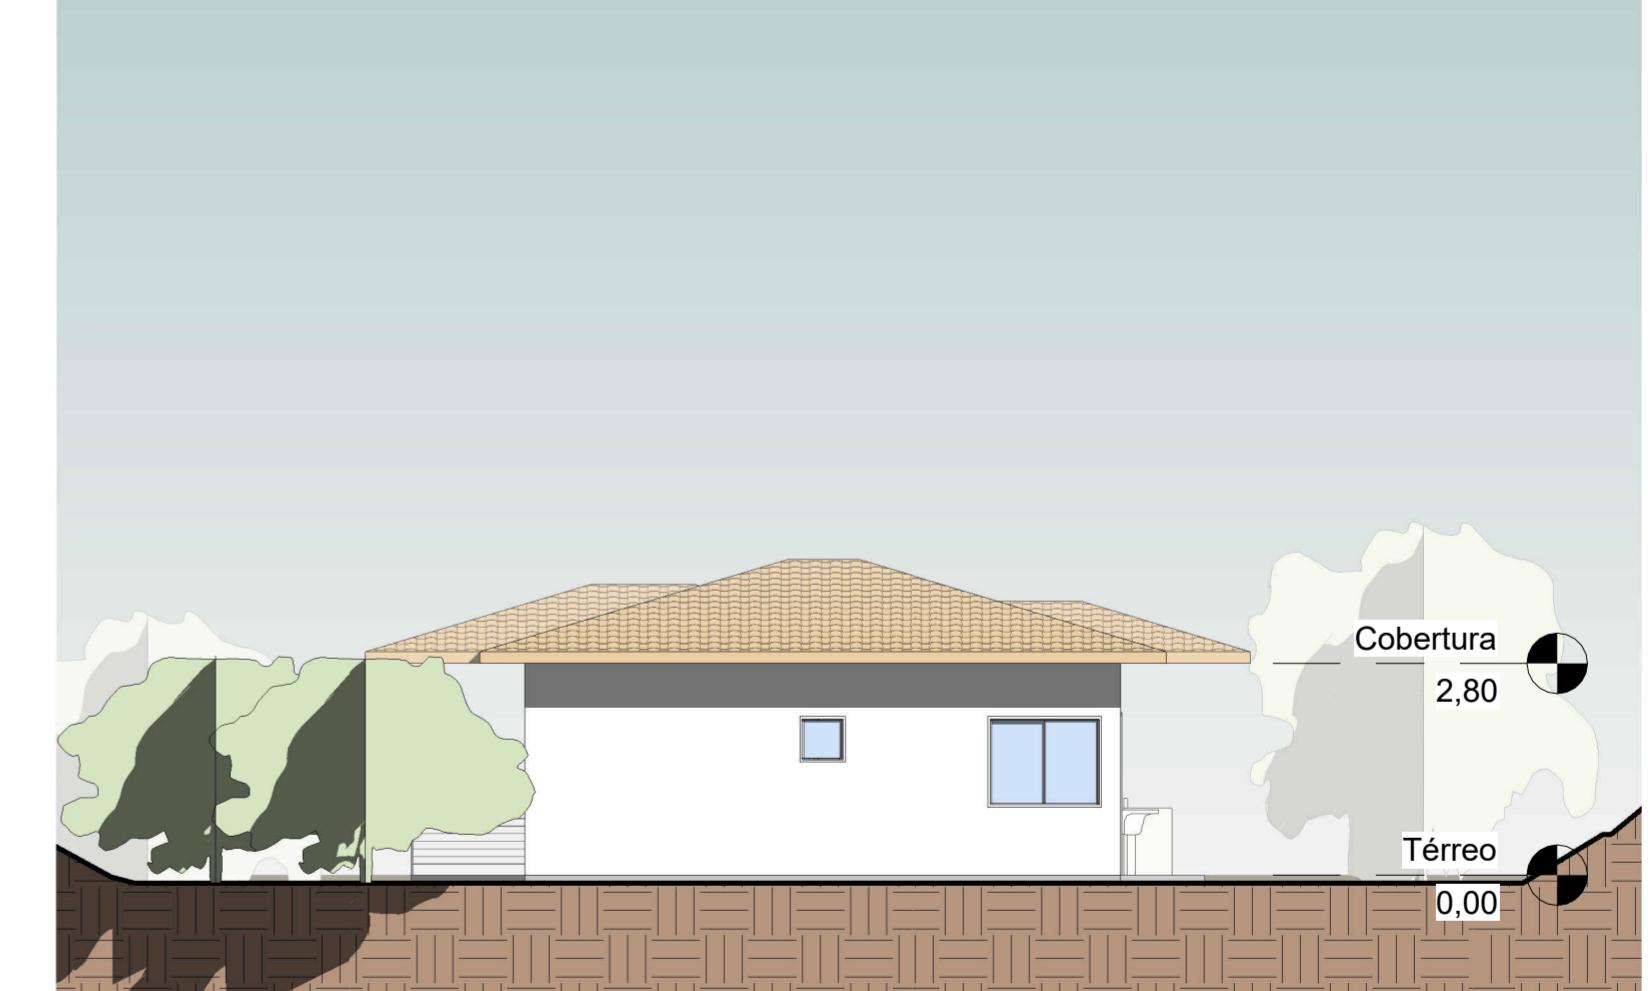


4 Elevação Norte
1 : 100

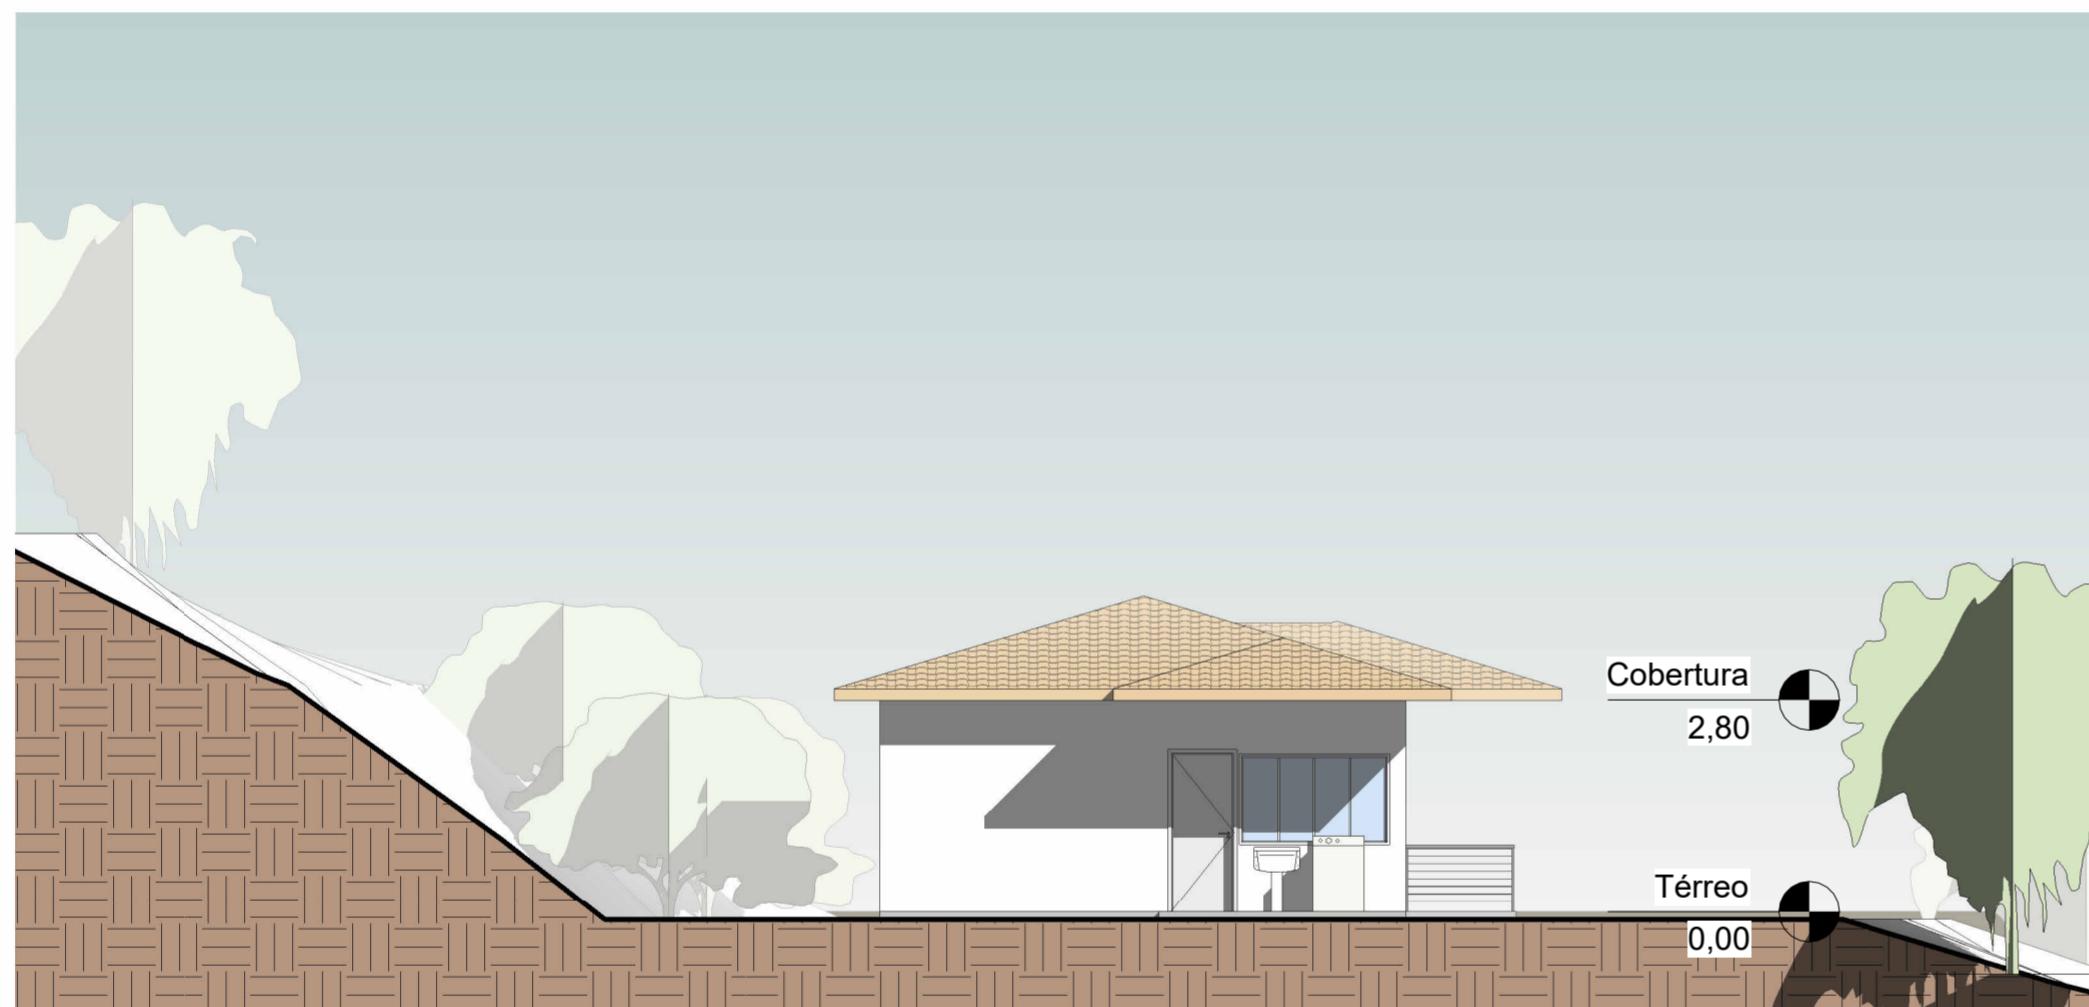

1 Elevação Oeste
1 : 100




2 Elevação Sul
1 : 100

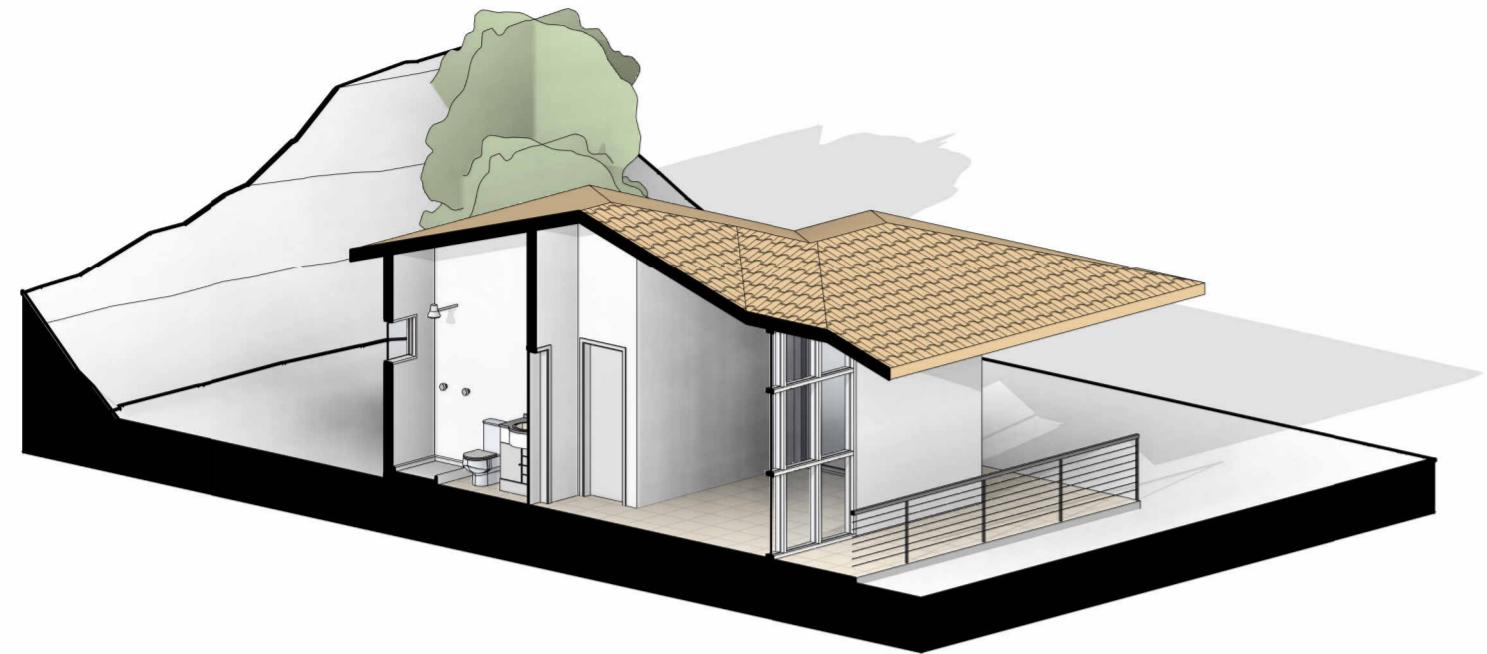

1 Perspectiva Seccionada 01



2 Perspectiva Externa

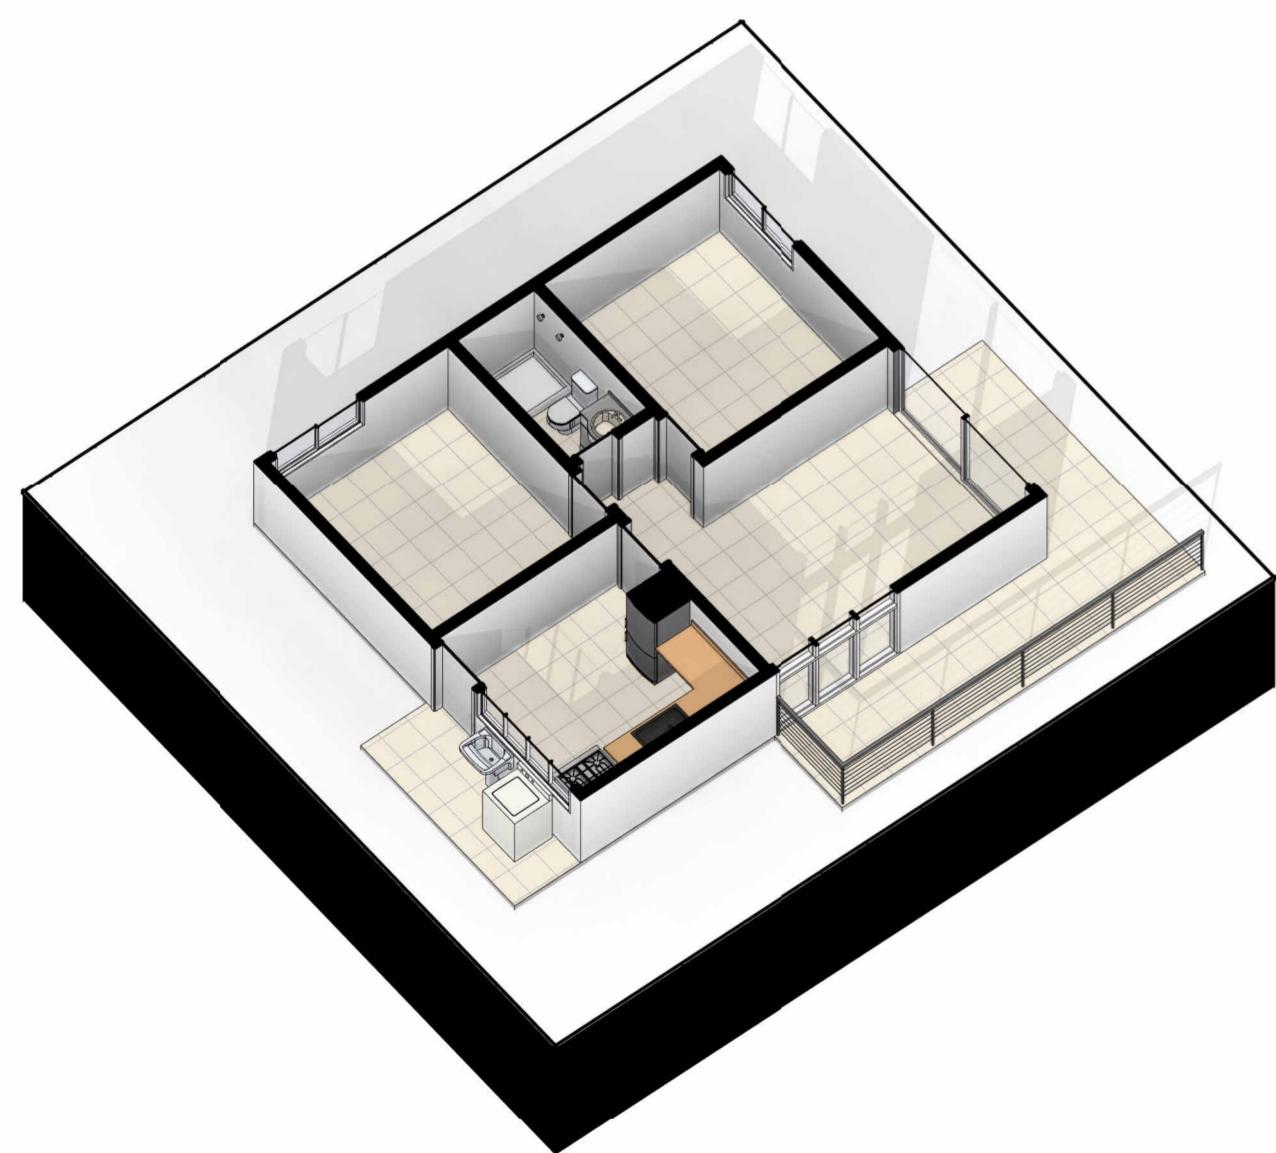

3 Perspectiva Seccionada 02



4 Perspectiva Interna

Axiom Treinamentos

Aula Experimental de Revit

Prof.: Erick Mark

00/00/0000

Perspectivas